

PROCES-VERBAL DE BORNAGE DE Morcellement du TF 10225K
CADASTRAL SURVEYS REPORT OF

L'an deux mille Vingt-ans le Vingt Mois de Février
In the year on the day of the month of
à dix heures.
at o'clock

Chandja O. Juste Prosper
Ingénieur Géomètre-Expert
N° 10355

Nous, soussigné :
I, the undersigned

Du cadastre dûment assermenté désigné pour procéder au bornage d'un immeuble bâti ou non bâti(1)
Of the department of surveys, appointed to mark out the boundaries of a developed (1) property situated at

lieu dit Nkoloulou III
in the place known as

Commune : Rural Arrondissement : Obala
Council Sub-division

Département : Lékou Région : Centre
Division Region

République du Cameroun, suivant demande (2) en date du
Republic of Cameroon, in accordance with application (2) date on
N° de M.: ABOU, C. et DRA B. yn Colette et ch
N° From M

Précédent du bornage de morcellement du TF 10225K daté
de 20/02/2025 au profit de M. NDAOUNY YONTA
JOSIE.

Nous nous sommes rendus sur les lieux, et en présence de :
Visited the property, in the presence of


De M.(3) ABOU, C. et DRA B. yn C. et ch (qualité) Propriétaires
Messrs(3) (Capacity)

et M. NDAOUNY YONTA JOSIE (acquéreur)

(1) Rayer la mention inutile
Delete where inapplicable

(2) Demande actes, jugements, décisions ou autres pièces officielles avec date
Application for deeds, judgements, decisions or other dated official documents


(3) Indiquer correctement l'identité : nom - prénoms - date de naissance et adresses s'il y a lieu.
Fill in the identity ; full name, date of birth and address if necessary

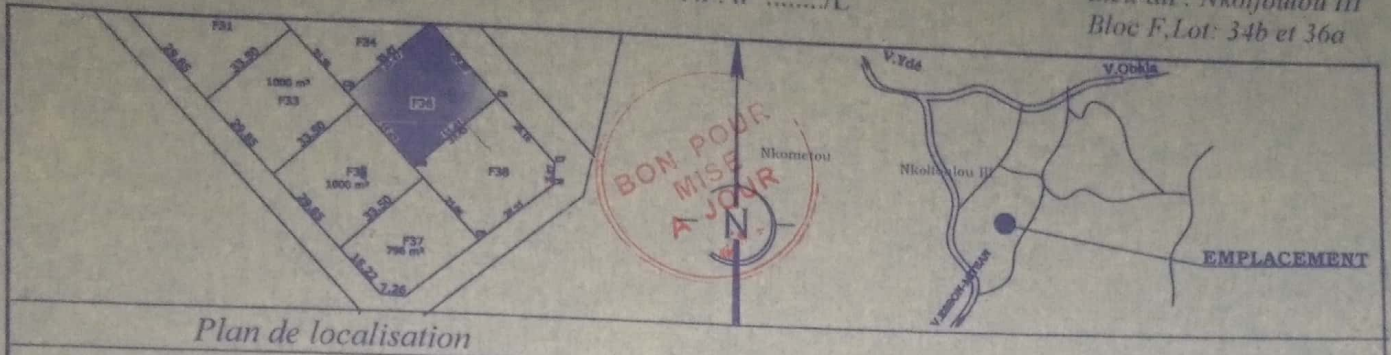

Plan de localisation

Plan joint au P.V de bornage de morcellement du T.F n° 10225/L établi le
20/02/2025 a la demande de Mme. ABOUDI epse OBA BIYA Colette et Cts au
profit de **M. NDOUNYO YONTA Josue**

$SUP = 1001m^2$

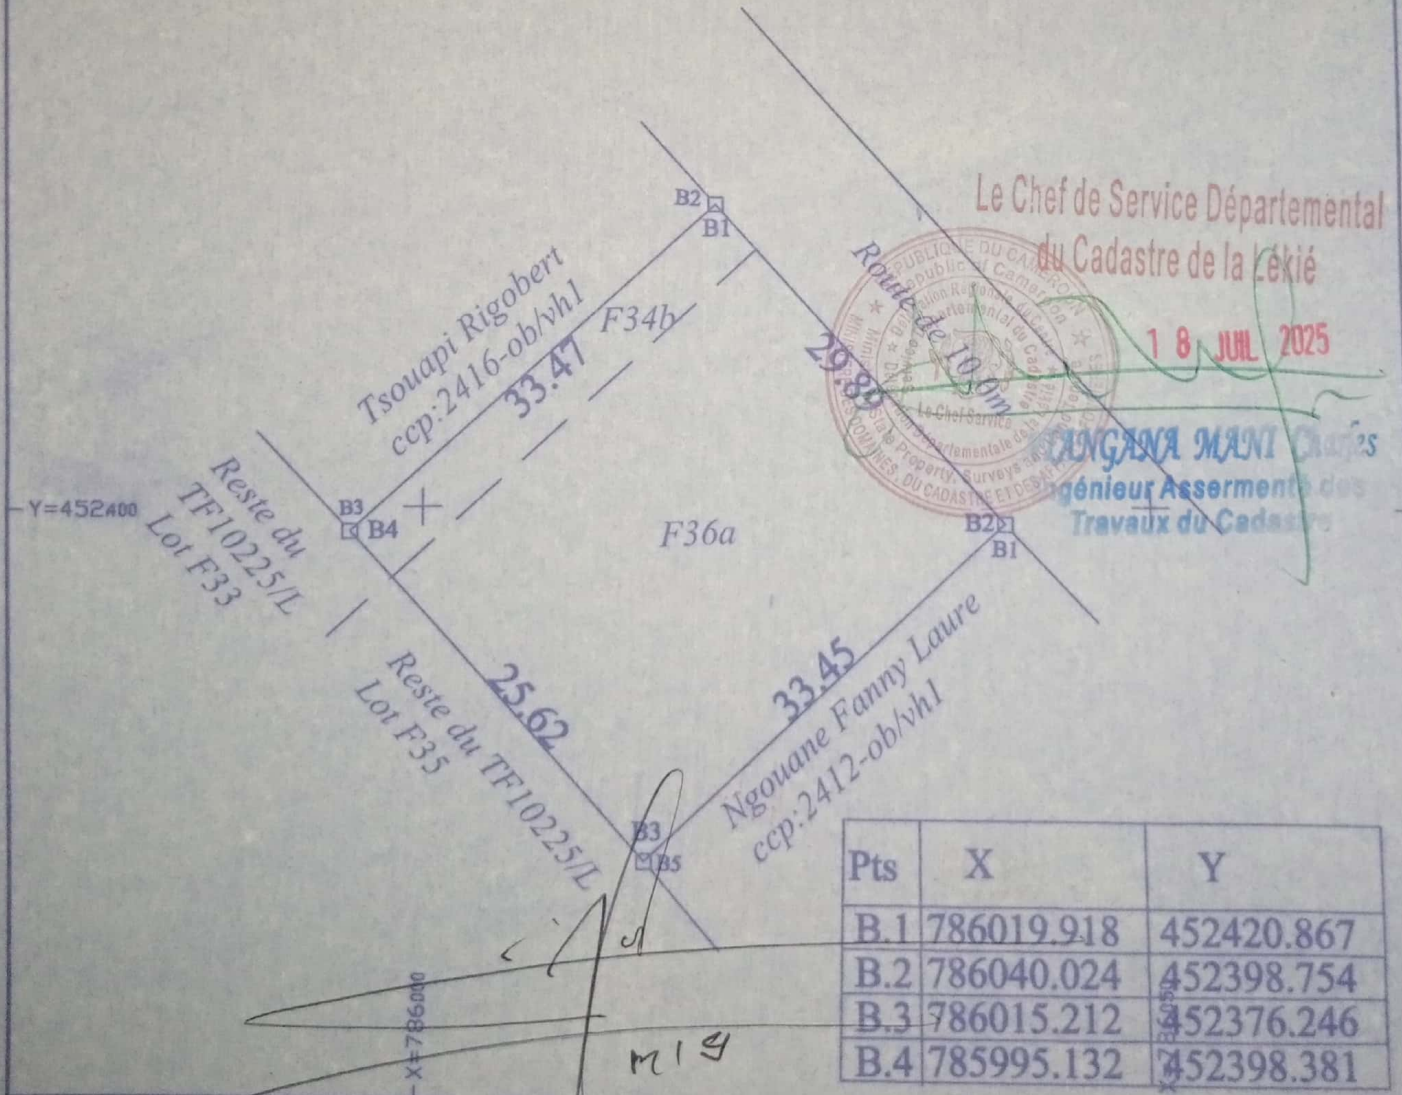

Pts	X	Y
B.1	786019.918	452420.867
B.2	786040.024	452398.754
B.3	786015.212	452376.246
B.4	785995.132	452398.381

Levé et dressé par M. OHANDJA
ONANA Juste Prosper
Geometre Expert agree a l'OGEC n° A055
OBALA le 20/02/2025

ECH : 1/500

Mappe de repérage au
R.G.N.C

C.C.P : 2414-OB/VH1

RV 008 2025
OHANDJA ONANA Juste P.
Geometre Expert-Clientèle Privée
NGES-DEP-...

ERREURS OU CONTESTATIONS (1) ERRORS OR COMPLAINTS (1)



Attendu qu'il ne s'est élève aucune contestation et qu'il n'a été constaté aucune erreur de désignation (autres que celles consignées ci-dessus) (2) , Nous avons clos et arrêté définitivement le présent procès-verbal pour servir et valoir ce que de droit, en présence des parties en cause lesquelles ont signé avec nous.


No complaint having been lodged and No description erro (2) having been discovered (other than those listed above (2) i drew up finally closed this report to serve for all purpose for which it may be needed in the presence of the interested parties who signed with me.

Fait et clos à Obala le 20/02/2025 Les jours, mois et an ci-dessus.
Done and closed at on the day, month and year above

Le(s) Réquérants
Owners of adjacent Property

L'Acquereur
Applicant

Le Géomètre
The Surveyor

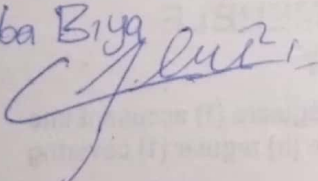
Aboudi Colette epse
Oba Brya


ETEME GILBERT

Le Chef de Service Départemental
du Cadastre de la Lékou



18 JUL 2025

(1) Préciser la nature des erreurs ou oppositions et la suite impartie
State nature of errors complaints and action taken

(2) Ajouter le cas échéant : " autres que celles consignées ci-dessus "
Add necessary " other those listed above "

OHANJA MONT Charles
Ingénieur Assermenté des
Travaux du Cadastre